




xgm-lite-frame floor plan 1:1 outside 270.7 x 248 mm (board origin = its rear/24-pin corner)

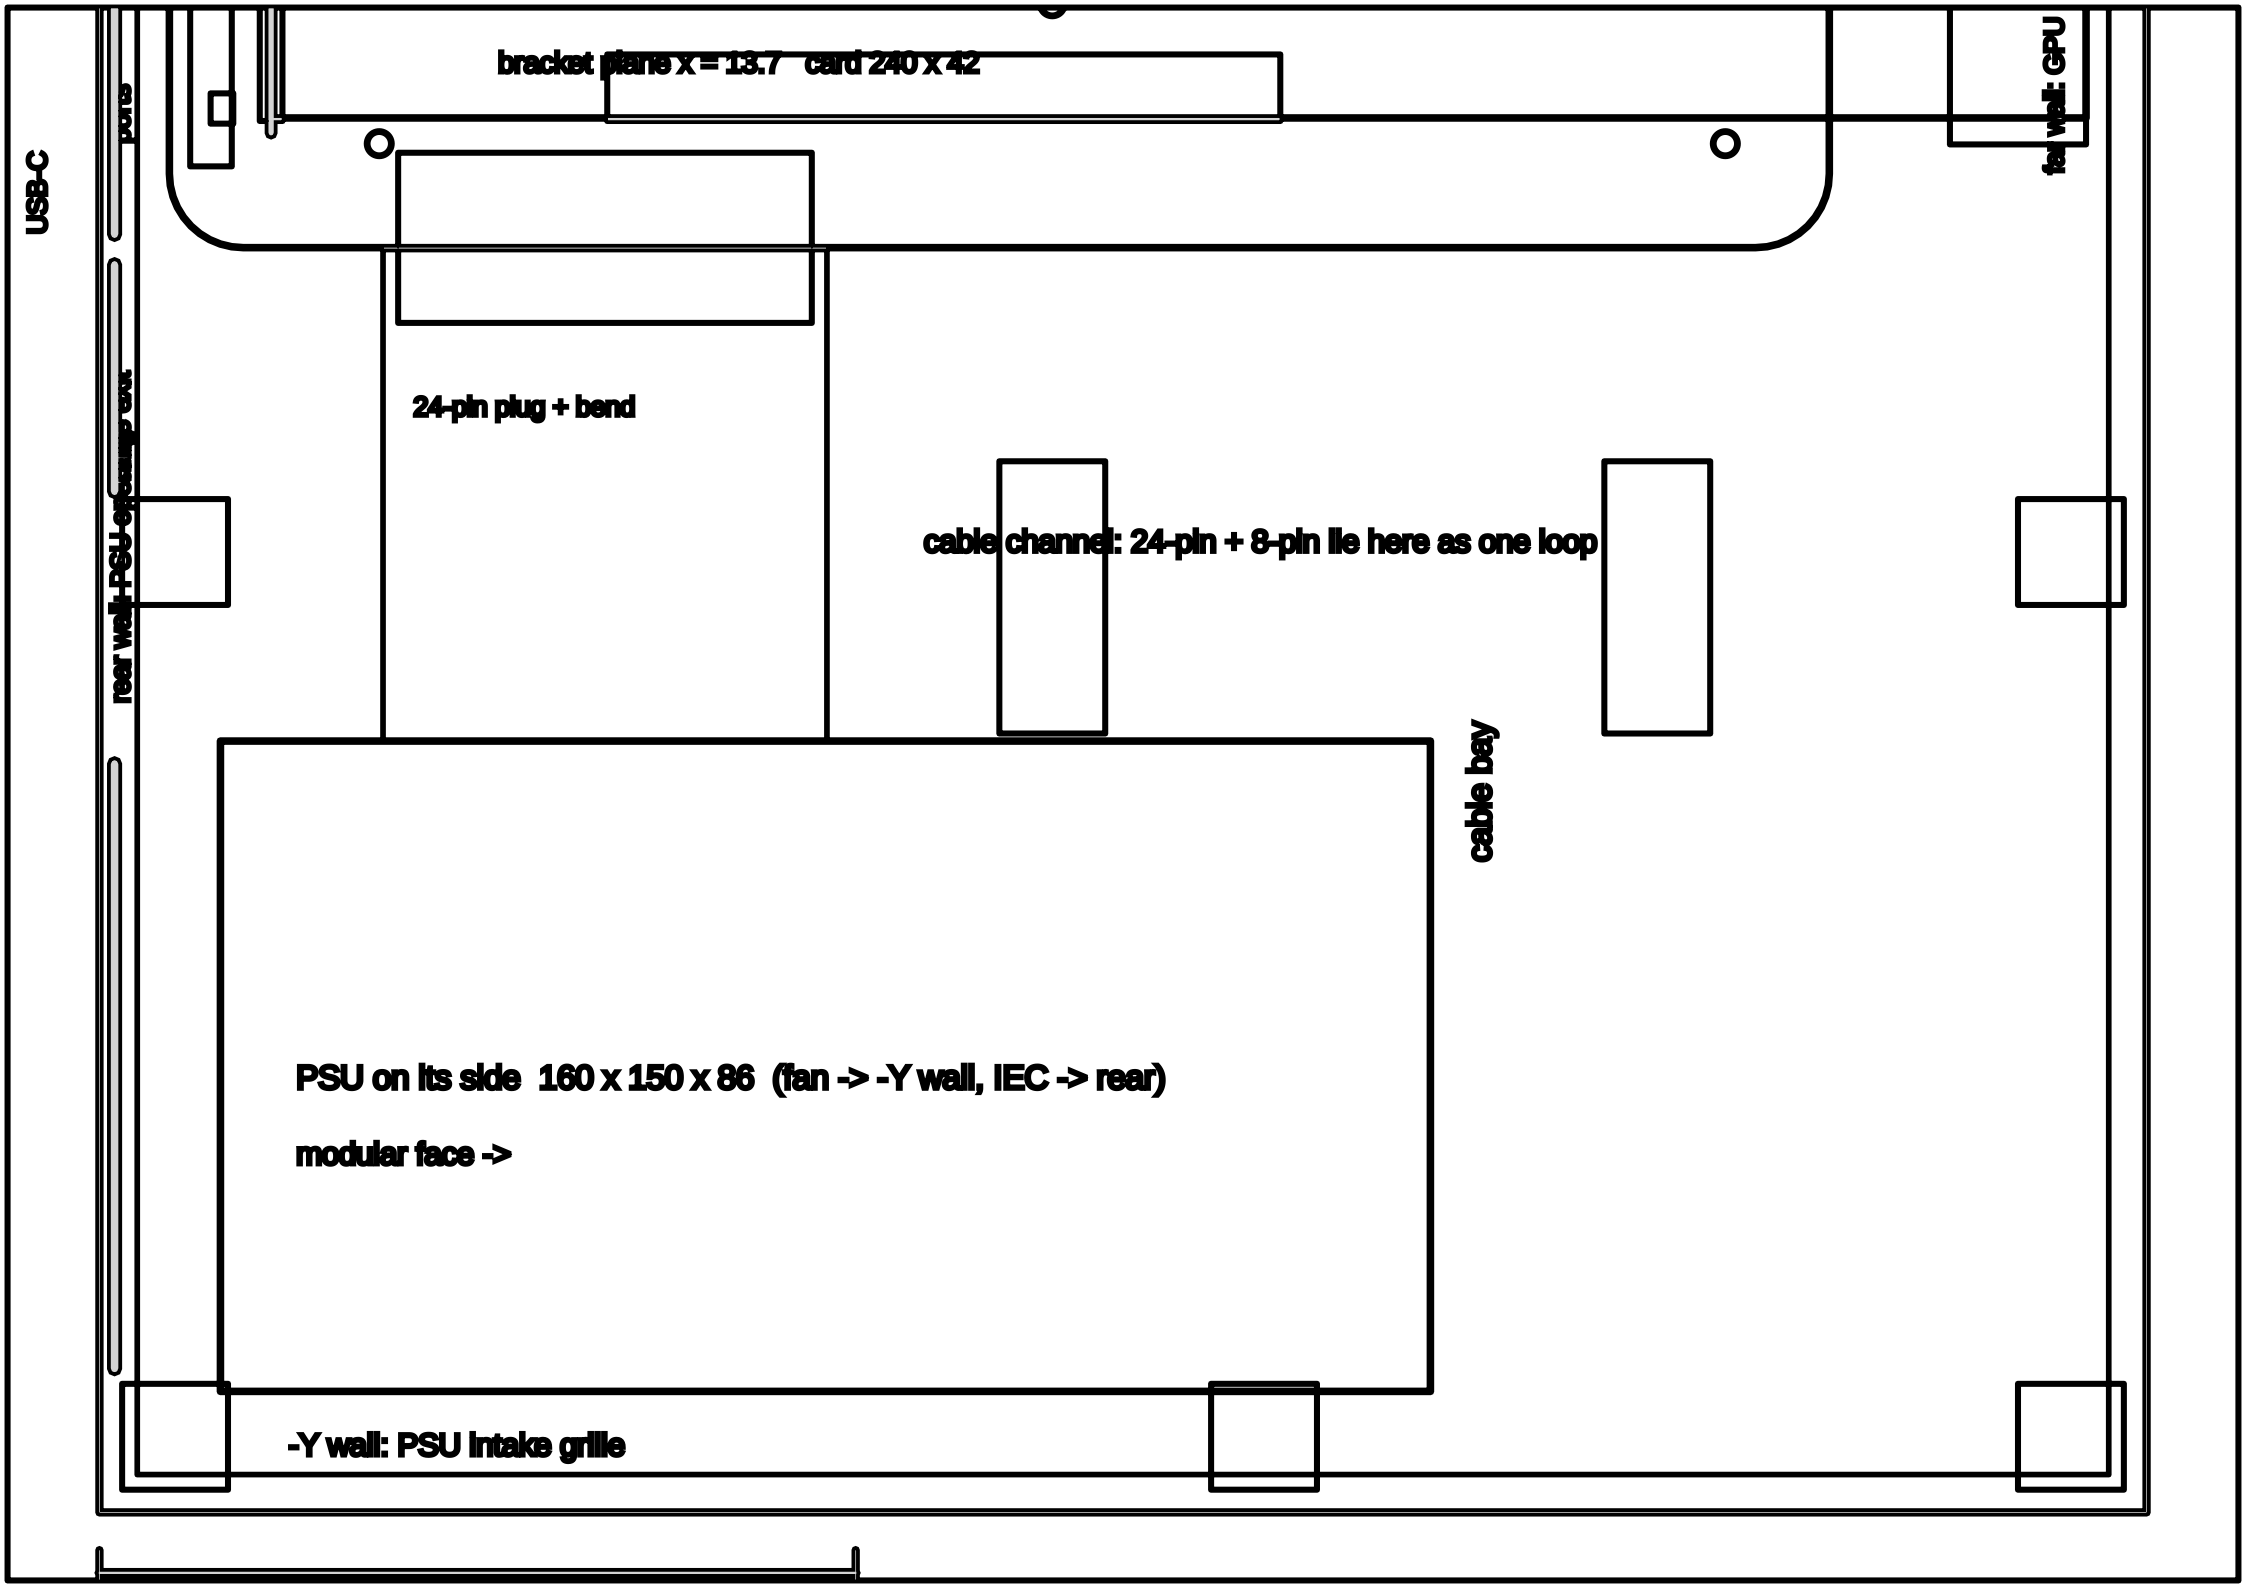